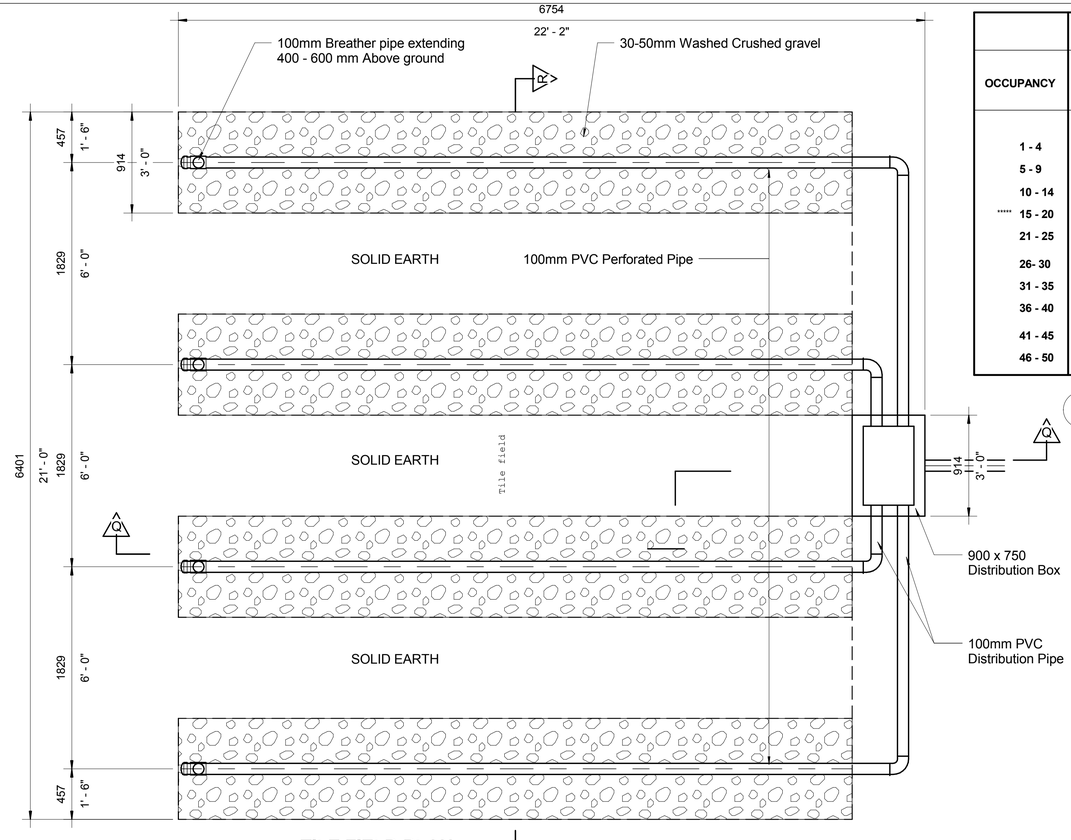

TILE FIELD PLAN

OCCUPANCY	SEPTIC TANK Capacity in Leters	Length A	Width B	Air Space C	Liquid Depth D	SIPHON TANK Length E	Width F	Depth G	CONCRETE Walls J	Top I	Bottom K
1 - 4	1500	1524	750	300	1050				150	100	150
5 - 9	2050	1800	750	300	1200	900	750	900	150	100	150
10 - 14	3250	2100	1050	300	1200	1050	1050	900	150	100	150
***** 15 - 20	4550	2400	1200	300	1200	1200	1200	900	150	100	150
21 - 25	5685	2700	1350	300	1275	1350	1350	900	200	125	150
26- 30	6730	2850	1400	375	1350	1400	1400	1050	200	125	150
31 - 35	7820	3000	1500	375	1400	1500	1500	1050	200	125	150
36 - 40	8870	3150	1575	375	1475	1575	1525	1050	225	125	150
41 - 45	9890	3300	1650	375	1500	1650	1650	1050	225	125	150
46 - 50	10910	3450	1675	375	1500	1675	1675	1050	225	125	150

7 SEPTIC TANK NOTES
1 : 50

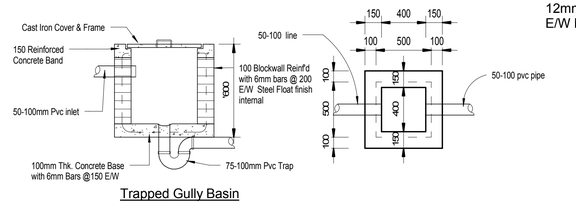

Trapped Gully Basin

5 Trapped Gully Basin
1 : 25

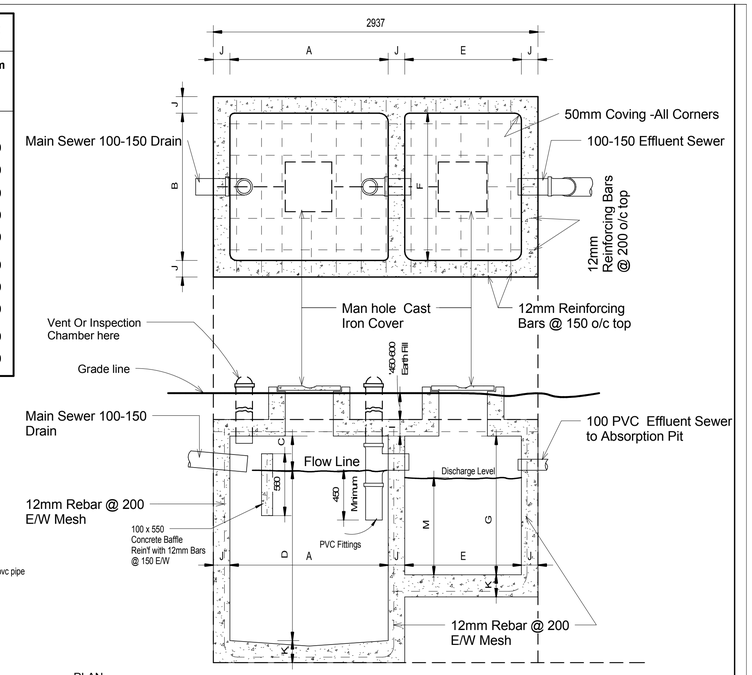

PLAN

3 Septic Tank
1 : 25

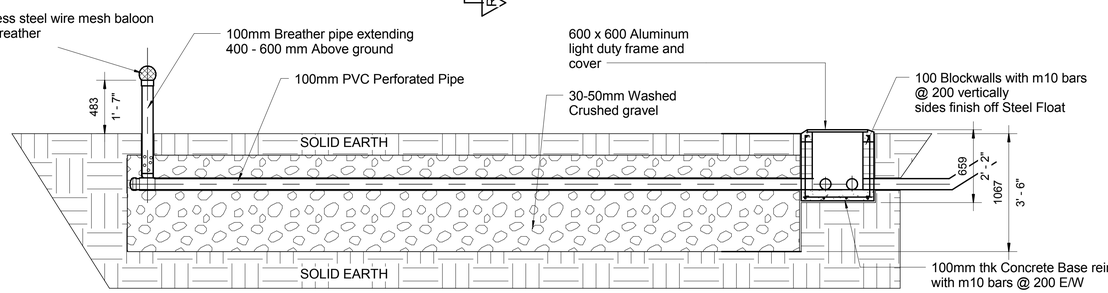

SECTION Q-Q

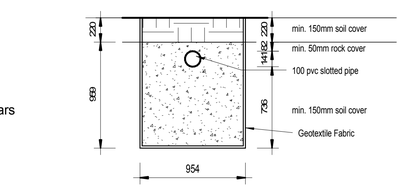

8 Tile Field Details
1 : 25

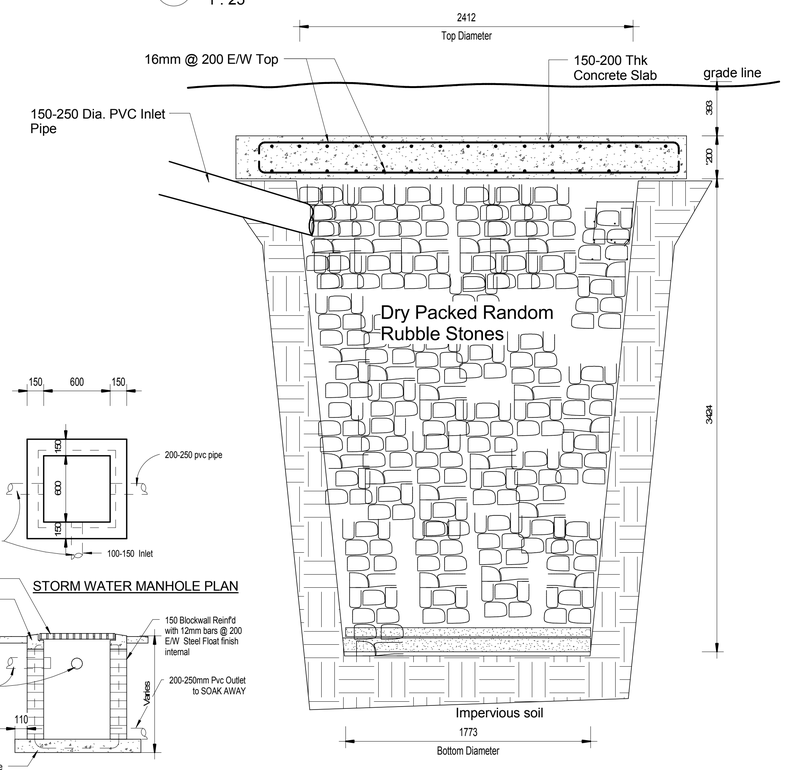

2 Storm Water Soak Away
1 : 20

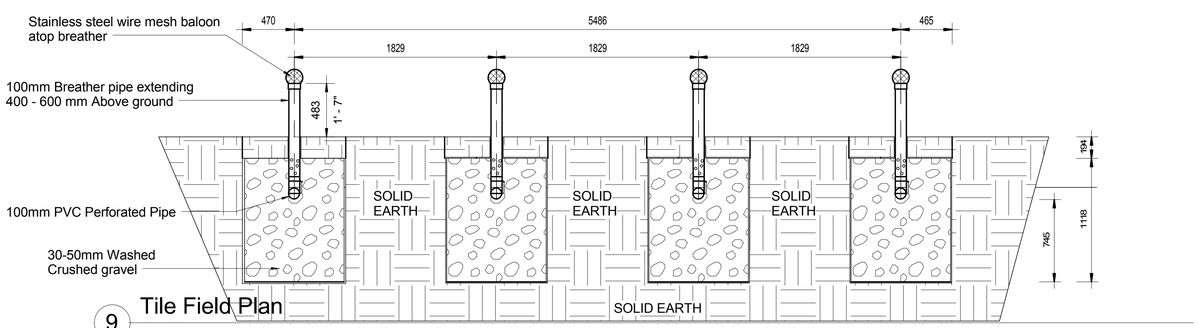

9 Tile Field Plan
1 : 25

SECTION R- R

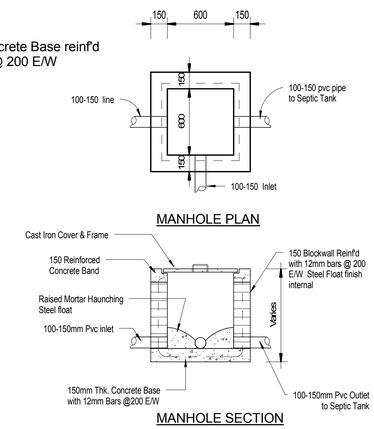

4 Manhole
1 : 25

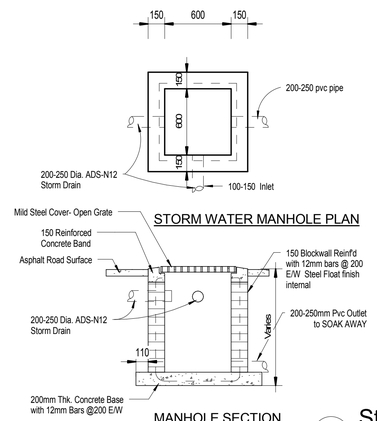

6 Storm Water Manhole
1 : 25

PROJECT NAME	LOCATION	SHEET TITLE	CLIENT'S	SIZE	DRAWN BY. Author	SIGN	REV.
PROPOSED RESIDENTIAL DEVELOPMENT		**DRAINAGE DETAILS**	ADDRESS Approver	Design I. Moncrieffe	DWG NO. **Det.D11010**	DATE.	
				CHECKED	SCALE As indicated	SHEET S9	